

Приложение №1
к договору №34К/23
от 29.09.2023 г.

ЭСКИЗНЫЙ ПРОЕКТ



Дачный дом
6,0х8,0м

2023 г.

Ведомость чертежей

Лист	Наименование	Примечание
1	Титульный лист	
2	Ведомость чертежей	
3	Фасад А-Д. Фасад Д-А	
4	Фасад 1-3. Фасад 3-1	
5	План первого этажа	
6	План второго этажа	
7	Разрез 1-1	
8	План фундамента	
9	План раскладки обвязочного бруса	
10	Схема привязки объекта к границам участка	
11	Ведомость окон	
12	Ведомость дверей	

Архитектурно-пространственное и функциональное решение


Дом спроектирован по каркасной технологии. Здание двухэтажное с террасой и балконом. Высота первого этажа - 2,4м, второго - 2,2м. Наружная отделка - имитация бруса. Окна ПВХ. Настил пола - шпунтованная доска. Кровля выполнена из металлочерепицы. Фундамент - забивные сваи.

Технико-экономические показатели


Размеры здания	6,0х8,0 м
Площадь застройки	48,0 м ²
Общая площадь помещений	52,6 м ²

				Приложение №1 к договору №34К/23 от 29.09.2023			
Заказчик							
ГИП				Ведомость чертежей	Стадия	Лист	Листов
					ЭП	2	12
Подряд.					ИП Калякин А.А.		
Проектир.							

Фасад А-Д

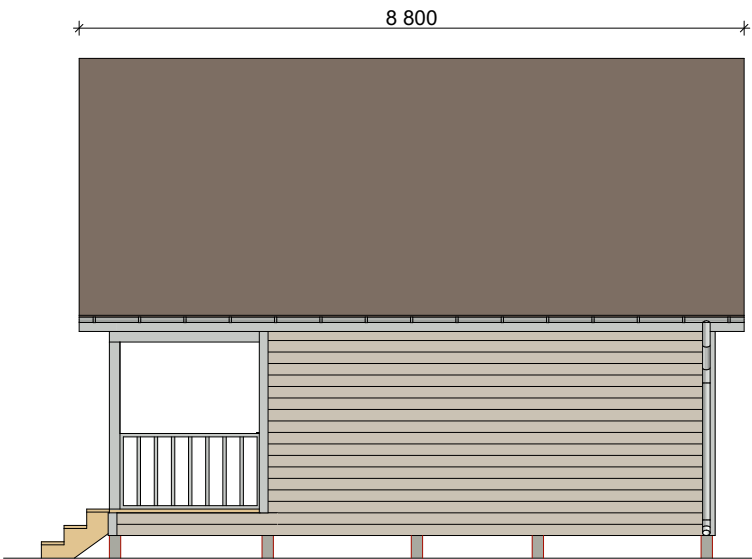


Фасад Д-А

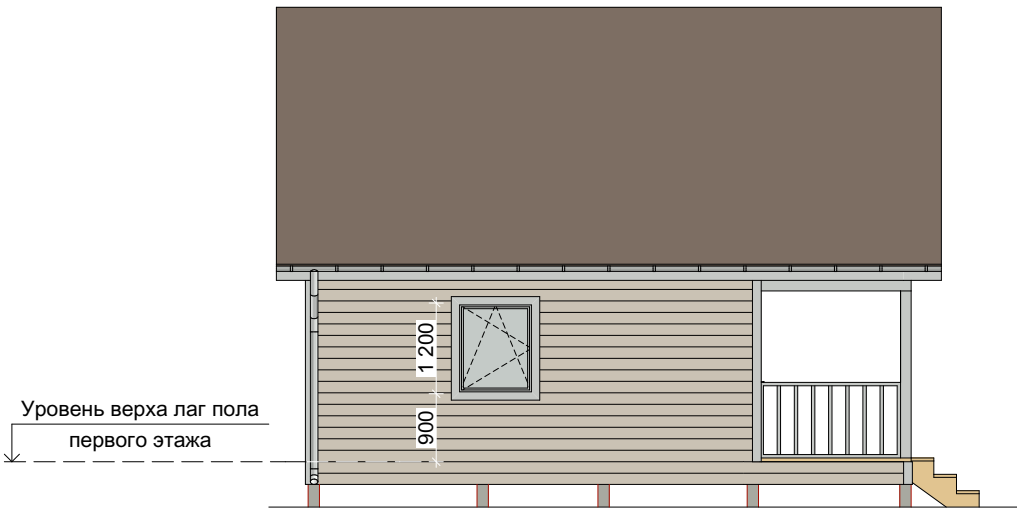


				Приложение №1 к договору №34К/23 от 29.09.2023			
Заказчик				Фасад А-Д. Фасад Д-А	Стадия	Лист	Листов
ГИП					ЭП	3	12
Подряд.					ИП Калякин А.А.		
Проектир.							

Фасад 1-3

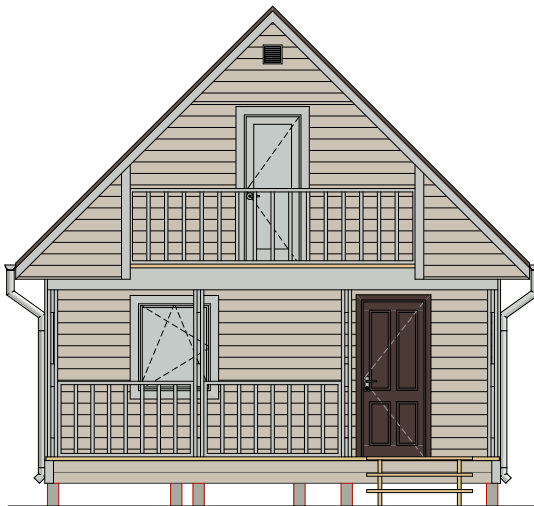


Фасад 3-1

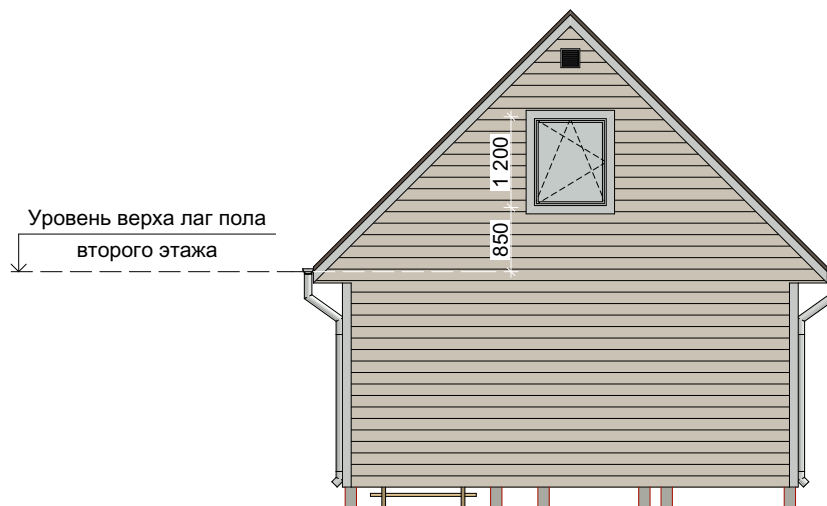

				Приложение №1 к договору №34К/23 от 29.09.2023			
Заказчик				Фасад 1-3. Фасад 3-1	Стадия	Лист	Листов
ГИП					ЭП	4	12
Подряд.					ИП Калякин А.А.		
Проектир.							

Примечание: размеры указаны по каркасу, без учета наружной и внутренней отделки


План первого этажа

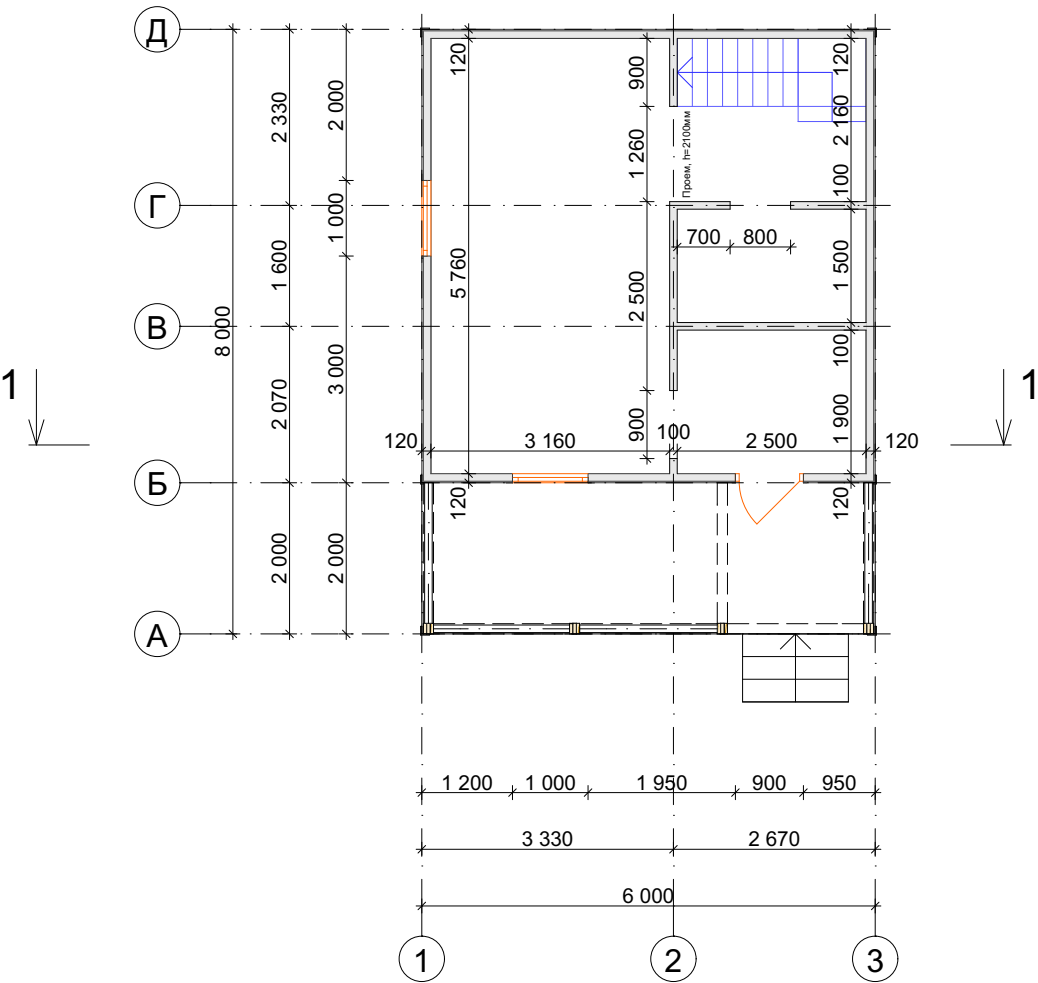

				Приложение №1 к договору №34К/23 от 29.09.2023			
Заказчик				План первого этажа	Стадия	Лист	Листов
ГИП					ЭП	5	12
Подряд.					ИП Калякин А.А.		
Проектир.							

Примечание: размеры указаны по каркасу, без учета наружной и внутренней отделки


План второго этажа

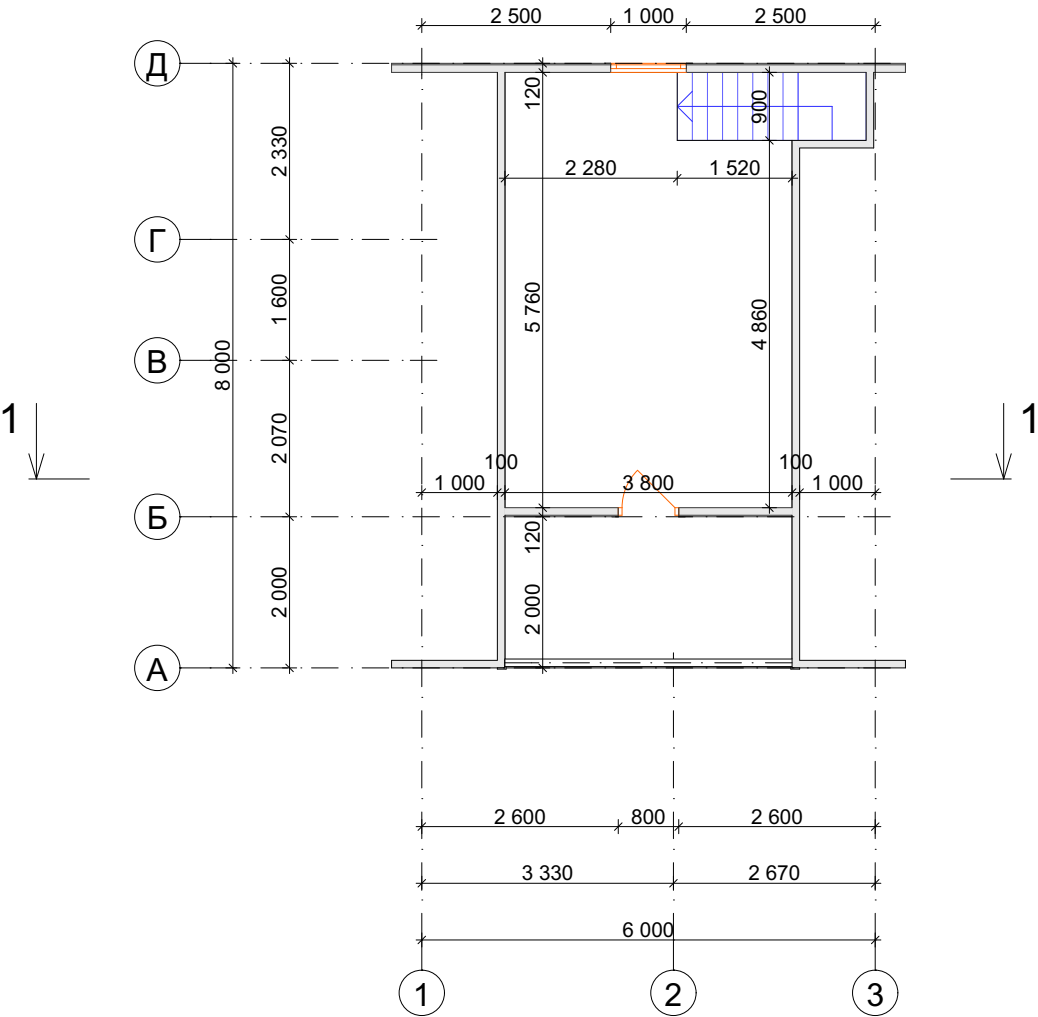


				Приложение №1 к договору №34К/23 от 29.09.2023			
Заказчик				План второго этажа	Стадия	Лист	Листов
ГИП					ЭП	6	12
Подряд.					ИП Калякин А.А.		
Проектир.							

Примечание: размеры указаны по каркасу, без учета наружной и внутренней отделки

Разрез 1-1

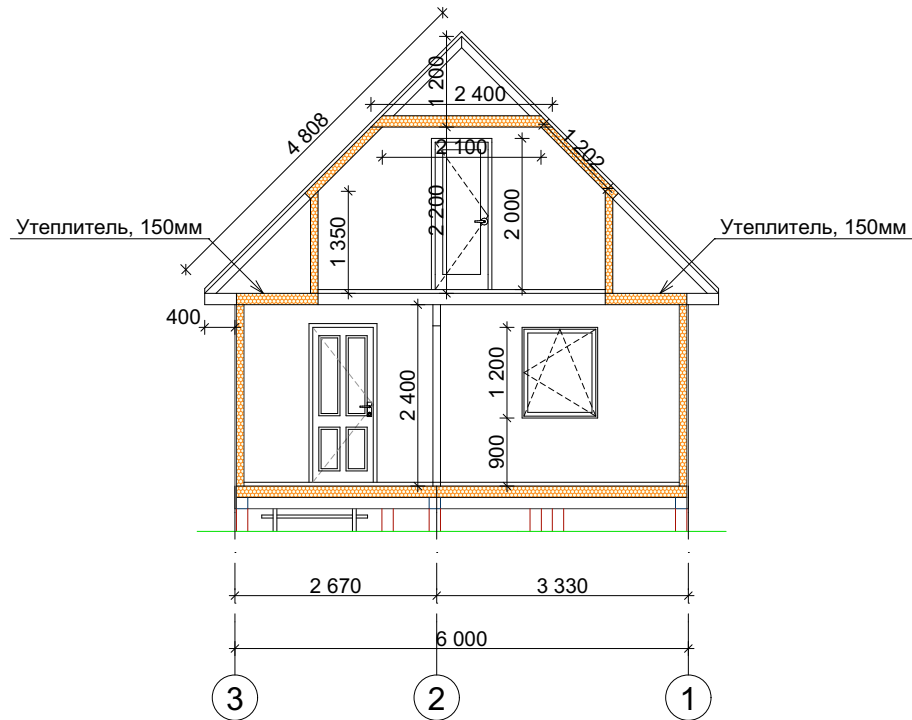


Разрез наружной стены

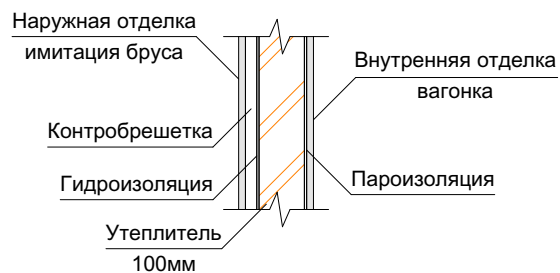


				Приложение №1 к договору №34К/23 от 29.09.2023			
Заказчик				Разрез 1-1	Стадия	Лист	Листов
ГИП					ЭП	7	12
Подряд.					ИП Калякин А.А.		
Проектир.							

План фундамента

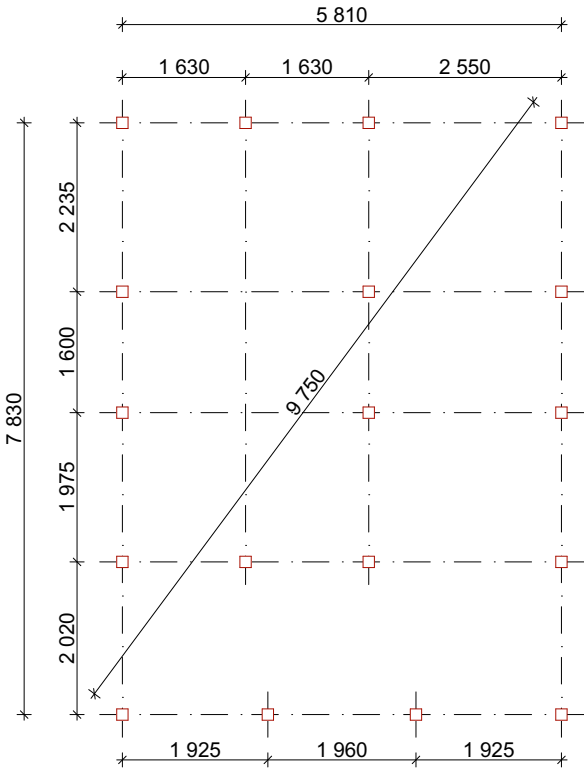


				Приложение №1 к договору №34К/23 от 29.09.2023			
Заказчик							
ГИП				План фундамента	Стадия	Лист	Листов
					ЭП	8	12
Подряд.					ИП Калякин А.А.		
Проектир.							

План раскладки обвязочного бруса

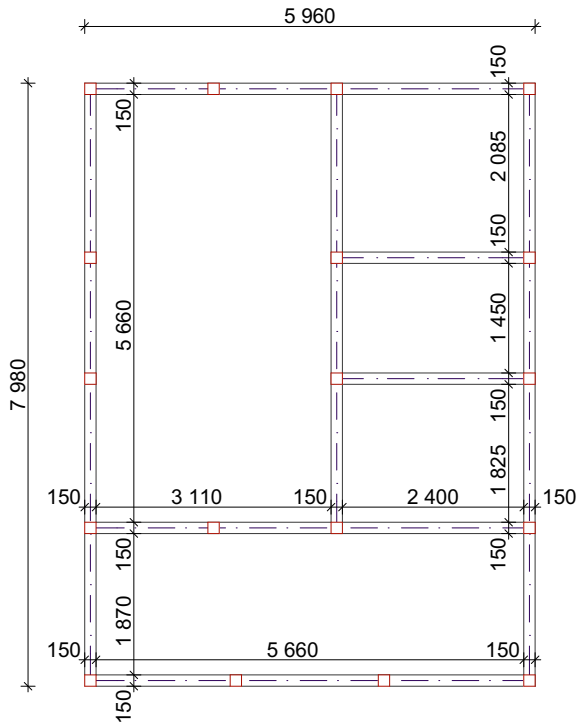

				Приложение №1 к договору №34К/23 от 29.09.2023			
Заказчик							
ГИП				План раскладки обвязочного бруса	Стадия	Лист	Листов
					ЭП	9	12
Подряд.					ИП Калякин А.А.		
Проектир.							

Схема привязки объекта к границам участка

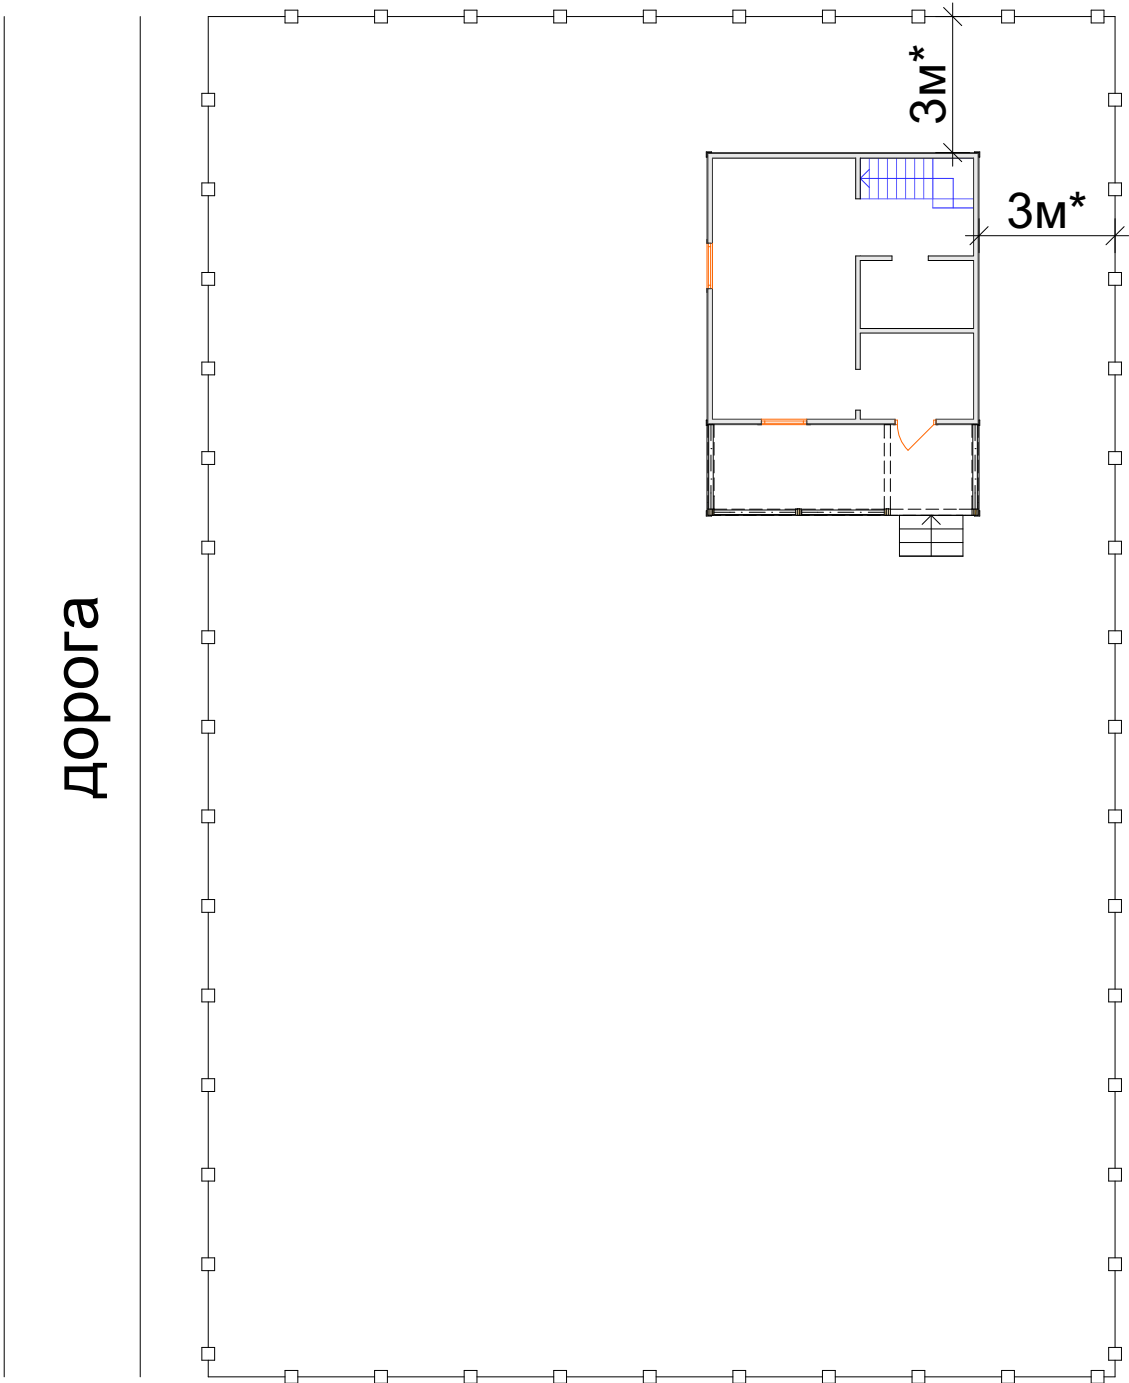


— □ — □ — - граница участка
* - размер уточнить

				Приложение №1 к договору №34К/23 от 29.09.2023			
Заказчик				Схема привязки объекта к границам участка	Стадия	Лист	Листов
ГИП					ЭП	10	12
Подряд.					ИП Калякин А.А.		
Проектир.							

Ведомость окон

Кол-во	Размеры по проему Ш x В	Вид изнутри	Примечание
3	1 000x1 200		

				Приложение №1 к договору №34К/23 от 29.09.2023			
Заказчик							
ГИП				Ведомость окон	Стадия	Лист	Листов
					ЭП	11	12
Подряд.					ИП Калякин А.А.		
Проектир.							

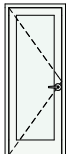Ведомость дверей									
Кол-во		Размеры по проему Ш x В		Вид со стороны открывания		Открывание двери		Примечание	
1		800x2 000				Внутрь, левая		ПВХ, без замка	
1		900x2 100				Наружу, правая		Металлическая, утепленная	

Приложение №2 к договору №34К/23 от 29.09.2023 г.

Комплектация

Фундамент

1. Фундамент - забивные сваи, 150х150х3000мм, 18шт.
2. Закрытие цоколя - отсутствует.
3. Отмостка - отсутствует.

Стеновой комплект

4. Обвязочный брус по фундаменту 150х150мм*, укладывается на гидроизоляцию (естественной влажности, нестроганный). Обработка антисептиком в 1 слой (при температуре ниже 0°C не производится).
5. Каркас наружных стен - доска 50х100мм*, шаг 590мм по краям, с укосинами (без обработки, естественной влажности, нестроганая).
6. Контробрешетка по наружному каркасу (наружная) - брусок 20х50мм* (вертикально, без обработки, естественной влажности, нестроганный). Наружная контробрешетка спускается до уровня низа цоколя.
7. Контробрешетка по наружному каркасу (внутренняя) - отсутствует.
8. Каркас перегородок - доска 50х100мм*, шаг 590мм по краям (без обработки, естественной влажности, нестроганая).
9. Опорные столбы террасы из двух досок 2х(45х140мм*) с тремя проставками между ними 300х45х140мм* (камерной сушки, строганая).
Верхняя обвязка столбов террасы из трех досок 3х(45х140мм*), камерной сушки, строганые.

Перекрытие

10. Черновой пол - обрезная доска 25х100мм*, шаг 350мм по краям (второй сорт, без обработки, естественной влажности, нестроганая).
11. Сетка от грызунов металлическая по полу первого этажа с заходом на наружные стены на 0,5м.
12. Лаги пола первого этажа - доска 50х150мм*, шаг 590мм по краям (естественной влажности, нестроганая). Обработка антисептиком в 1 слой (при температуре ниже 0°C не производится).
13. Лаги пола второго этажа - доска 50х150мм*, шаг 590мм по краям (без обработки, естественной влажности, нестроганая).

Кровельная система

14. Стропильная система - доска 50х150мм*, шаг 590мм по краям (без обработки, естественной влажности, нестроганая).
15. Контробрешетка - брусок 20х50мм*, с зазором 100-150мм (без обработки, естественной влажности, нестроганный).
16. Обрешетка - доска 25х100мм*, шаг 350мм (без обработки, естественной влажности, нестроганая).
17. Покрытие кровли - металлочерепица 0,45мм (цвет - RAL 8017).
18. Торцевые и карнизные планки - металлические (цвет - RAL 8017).
19. Водосточная система ПВХ на металлических кронштейнах - желоба по 2 скатам, 2 трубы (цвет - белый).
20. Снегозадержатели - отсутствуют.

Утепление

21. Утепление пола первого этажа - рулонная минеральная вата 150мм (ISOVER/KNAUF).
22. Утепление межэтажного перекрытия - отсутствует.
Утепление межэтажного перекрытия по периметру наружных стен дома - рулонная минеральная вата 150мм (ISOVER/KNAUF).
23. Утепление потолка второго этажа (по затяжкам у стропил) - рулонная минеральная вата 150мм (ISOVER/KNAUF).
Утепление скатов кровли второго этажа (до затяжек у стропил) - плитная минеральная вата 150мм (ISOVER/KNAUF, низкой плотности).
24. Утепление наружных стен первого и второго этажа - плитная минеральная вата 100мм (ISOVER/KNAUF, низкой плотности).
25. Утепление перегородок первого и второго этажа - отсутствует.
26. Гидроизоляция (по черновому полу первого этажа, наружные стены первого и второго этажа) - мембранная пленка АРДМАНол А.
27. Пароизоляция (наружные стены первого и второго этажа, пол первого этажа, потолок первого этажа, потолок второго этажа) - мембранная пленка АРДМАНол В.
28. Гидроизоляция кровли - мембранная пленка АРДМАНол АS.

Примечание: * - погрешность по сечению пиломатериала ±5мм

				Приложение №2 к договору №34К/23 от 29.09.2023			
Заказчик							
ГИП				Комплектация	Стадия	Лист	Листов
					ЭП	1	3
Подряд.					ИП Калякин А.А.		
Проектир.							

Наружная отделка

29. Наружная отделка - имитация бруса, 138мм±2мм (2-6м, хвоя, сорт АБ, камерной сушки, крепление вразбежку без стыковочных планок).

Углы закрываются калиброванной доской 16х110±2мм (2-6м, камерной сушки).

30. Подшивка карнизов - имитация бруса, 16х110мм±2мм (2-6м, хвоя, сорт АБ, камерной сушки, крепление вразбежку без стыковочных планок). Во фронтонных частях монтируется перпендикулярно дому.

Подшивка потолка балкона - имитация бруса, 16х110мм±2мм (2-6м, хвоя, сорт АБ, камерной сушки, крепление вразбежку без стыковочных планок).

Подшивка потолка террасы - имитация бруса, 16х110мм±2мм (2-6м, хвоя, сорт АБ, камерной сушки, крепление вразбежку без стыковочных планок). В зоне под балконом шип срезается.

31. Настил пола террасы и балкона - деревянная террасная доска (без обработки).

Внутренняя отделка первого этажа

32. Внутренняя отделка наружных стен первого этажа - вагонка (2-3м, хвоя, сорт АБ, камерной сушки, без обработки, крепление вразбежку без стыковочных планок).

33. Отделка перегородок первого этажа - вагонка (2-3м, хвоя, сорт АБ, камерной сушки, без обработки, крепление вразбежку без стыковочных планок).

34. Отделка потолка первого этажа - вагонка (2-3м, хвоя, сорт АБ, камерной сушки, без обработки, крепление вразбежку без стыковочных планок).

35. Настил пола первого этажа - шпунтованная доска 28±2мм (3-6м, камерной сушки, без обработки).

36. Плинтуса по полу первого этажа - отсутствуют.

37. Плинтуса по стенам и потолку первого этажа - отсутствуют.

Внутренняя отделка второго этажа

38. Внутренняя отделка наружных стен второго этажа - вагонка (2-3м, хвоя, сорт АБ, камерной сушки, без обработки, крепление вразбежку без стыковочных планок).

39. Отделка перегородок второго этажа - вагонка (2-3м, хвоя, сорт АБ, камерной сушки, без обработки, крепление вразбежку без стыковочных планок).

40. Отделка потолка второго этажа (по затяжкам у стропил) - вагонка (2-3м, хвоя, сорт АБ, камерной сушки, без обработки, крепление вразбежку без стыковочных планок).

Отделка скатов кровли второго этажа (до затяжек у стропил) - вагонка (2-3м, хвоя, сорт АБ, камерной сушки, без обработки, крепление вразбежку без стыковочных планок).

41. Настил пола второго этажа - шпунтованная доска 28±2мм (3-6м, камерной сушки, без обработки).

42. Плинтуса по полу второго этажа - отсутствуют.

43. Плинтуса по стенам, скатам кровли и потолку второго этажа - отсутствуют.

Окна

44. Окна ПВХ 1,0х1,2м - 3шт. (размер указан по проему, двухкамерный стеклопакет, одностворчатые, белые, с поворотно-откидным механизмом).

45. Отливы на все окна - белые (низ), ширина 80мм.

46. Откосы внутри дома выполнены из внутренней отделки.

47. Подоконники выполнены из внутренней отделки.

48. Наличники снаружи дома - калиброванная доска 16х110±2мм (2-6м, камерной сушки).

49. Наличники внутри дома - планкен 19х95±2мм (2-6м, без обработки, камерной сушки).

Двери

50. Дверь входная металлическая, утепленная, пр-во Россия - 1шт. (бежевая изнутри)

51. Двери межкомнатные - отсутствуют.

52. Дверь балконная ПВХ 0,8х2,0м - 1шт. (размер указан по проему, белая, полностью стекло, двухкамерный стеклопакет, с доборным профилем со стороны петель, с поворотным механизмом, открывание внутрь, левая, с фурнитурой, без замка). Откосы внутри дома выполнены из внутренней отделки. Наличники снаружи дома - калиброванная доска 16х110±2мм (2-6м, камерной сушки). Наличники внутри дома - планкен 19х95±2мм (2-6м, без обработки, камерной сушки).

Примечание: * - погрешность по сечению пиломатериала ±5мм

				Приложение №2 к договору №34К/23 от 29.09.2023			
Заказчик				Комплектация	Стадия	Лист	Листов
ГИП					ЭП	2	3
Подряд.					ИП Калякин А.А.		
Проектир.							

Элементы дома

53. Лестница межэтажная деревянная, Г-образная, неврезная, из доски 45х140мм*, без перил и ограждений (без обработки).
54. Сборка каркаса на металлические гвозди 200мм, 150мм, 120мм, 100мм, 70мм. А также саморезы 90мм, 75мм, 50мм.
55. Ограждение террасы и балкона - брусok 45х45мм*, шаг 200мм (камерной сушки, строганый); поручень - доска 45х140мм* (горизонтально, камерной сушки, строганая).
56. Лестница на террасу из обрезной доски (без обработки).
57. Решетки вентиляционные во фронтонах - 2шт.
58. Покраска имитации бруса наружной отделки (на производстве): 1й слой - грунт с колером, 2й слой - покрытие укрывными красками Текнос (цвет - RAL 1013). Подкрас запилов производится по месту на объекте.
- Покраска углов, наличников (снаружи дома), карнизов и потолка террасы и балкона, столбов и верхней обвязки столбов террасы, ограждений террасы и балкона (на производстве): 1й слой - грунт с колером, 2й слой - покрытие укрывными красками Текнос (цвет - белый). Подкрас запилов производится по месту на объекте.

Организационные вопросы

59. Доставка. Удовлетворительное состояние подъездных путей до объекта обеспечивает Заказчик. Перенос строительного материала от места разгрузки до места строительства не более 15м.
60. Аренда бытовки на срок строительства.
61. Техническую и питьевую воду предоставляет Заказчик.
62. Электроэнергию предоставляет Заказчик.

Примечание: * - погрешность по сечению пиломатериала $\pm 5\text{мм}$

				Приложение №2 к договору №34К/23 от 29.09.2023			
Заказчик				Комплектация			
ГИП							
Подряд.							
Проектир.							
				Стадия	Лист	Листов	
				ЭП	3	3	
				ИП Калякин А.А.			